
David Poveda
23207-909595 CND

Lote 2
7.151,69 m2
ÁREA ÚTIL DESTINACIÓN VIP

PLANTA GENERAL PRIMER PISO

ETAPA 1 ESCALA 1 : 200

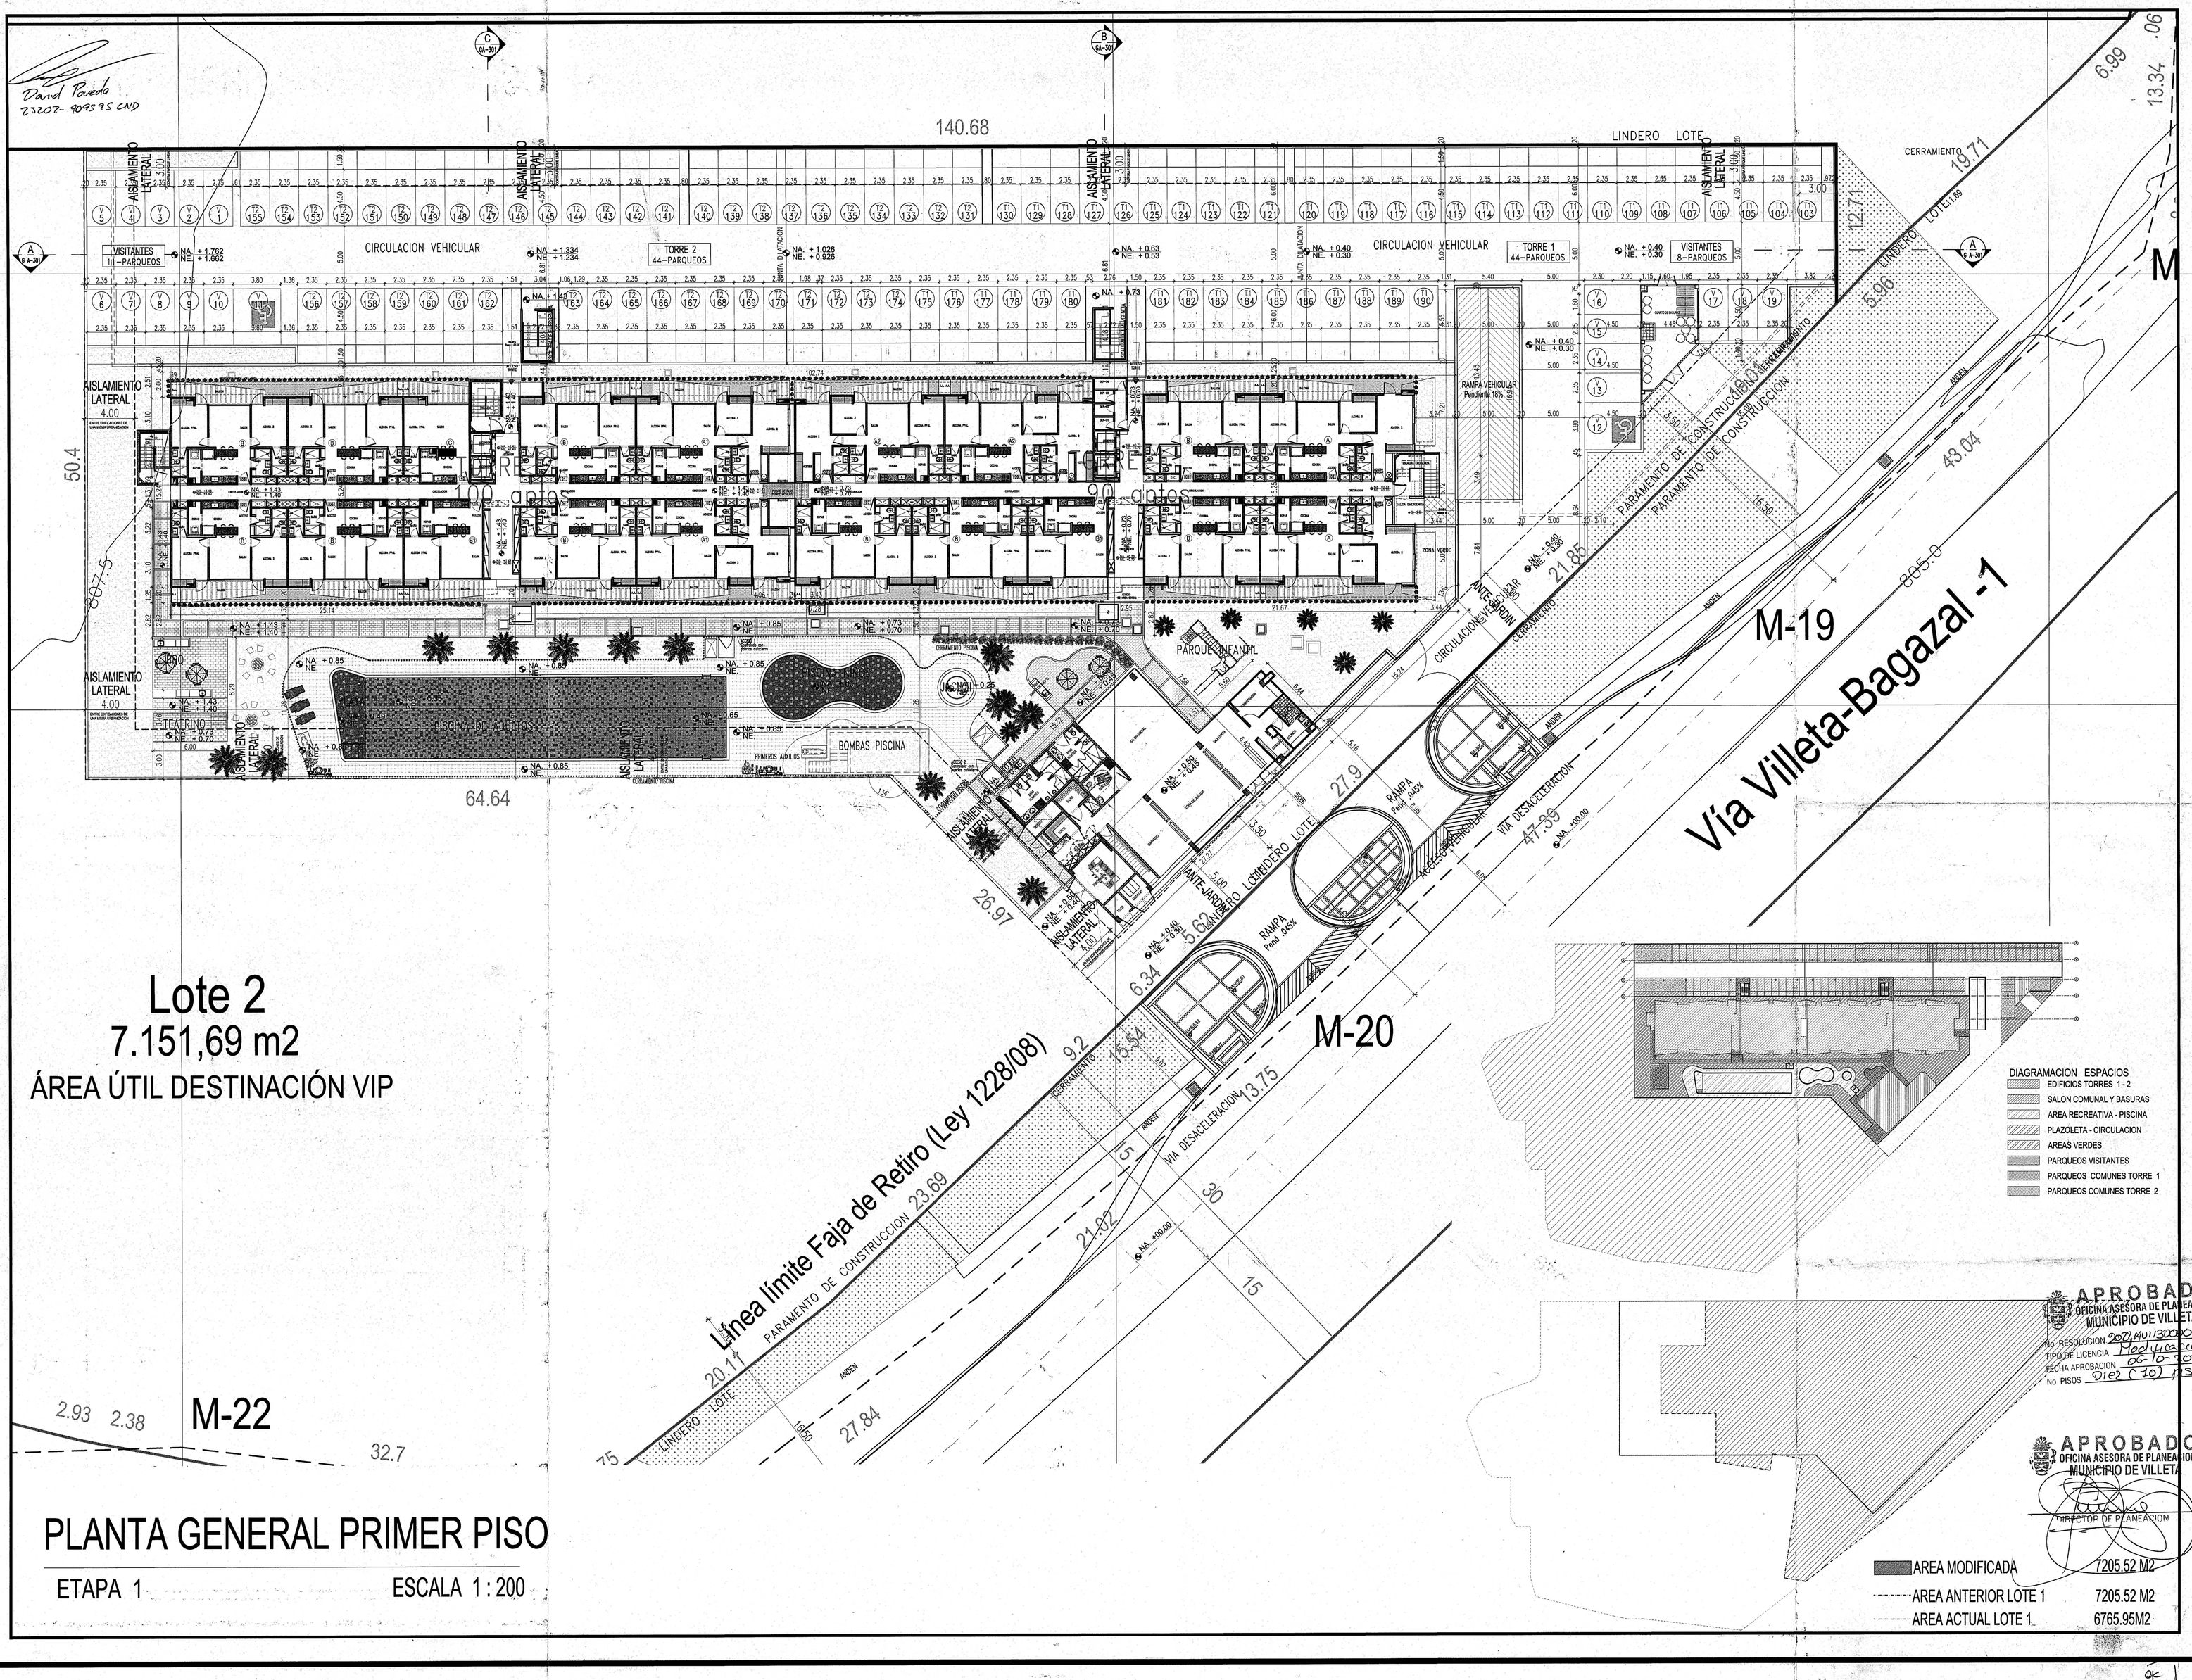

DIAGRAMACION ESPACIOS
- EDIFICIOS TORRES 1 - 2
- SALON COMUNAL Y BASURAS
- AREA RECREATIVA - PISCINA
- PLAZOLETA - CIRCULACION
- AREAS VERDES
- PARQUEOS VISITANTES
- PARQUEOS COMUNES TORRE 1
- PARQUEOS COMUNES TORRE 2

APROBADO
OFICINA ASESORA DE PLANEACION
MUNICIPIO DE VILLETA
No RESOLUCION 2020411200052182
TIPO DE LICENCIA Modificación
FECHA APROBACION 06-10-2020
No PISOS 01e2 e70 pisos

APROBADO
OFICINA ASESORA DE PLANEACION
MUNICIPIO DE VILLETA
DIRECTOR DE PLANEACION

AREA MODIFICADA	7205.52 M2
AREA ANTERIOR LOTE 1	7205.52 M2
AREA ACTUAL LOTE 1	6765.95M2

REV.	FECHA	OBSERVACIONES

REV.	FECHA	MODIFICACIONES	DIBUJO

actual colombia

GO arq Ospina García

NATIVA club
APARTAMENTOS/
Un estilo de vida inspirador

MODIFICACION DE LICENCIA VIGENTE

PROPIETARIO:
ACTUAL CONSTRUCTORA S.A.S.

RUT: 900439672-1

REPRESENTANTE LEGAL

DISEÑO:
ARQ. CARLOS OSPINA
Mat: 25700 26810 CND

PROYECTO:
NATIVA CLUB VILLETA

CONTENIDO:
LOTE 1
PLANTA GENERAL PRIMER PISO

ESCALA:	1 : 250
FECHA:	NOV-20-2020
PROYECTO: 1559	DIBUJÓ: E.G.G.
Nº PLANO: **R-G-A-102**	VERSION: 1
DE: 20	